


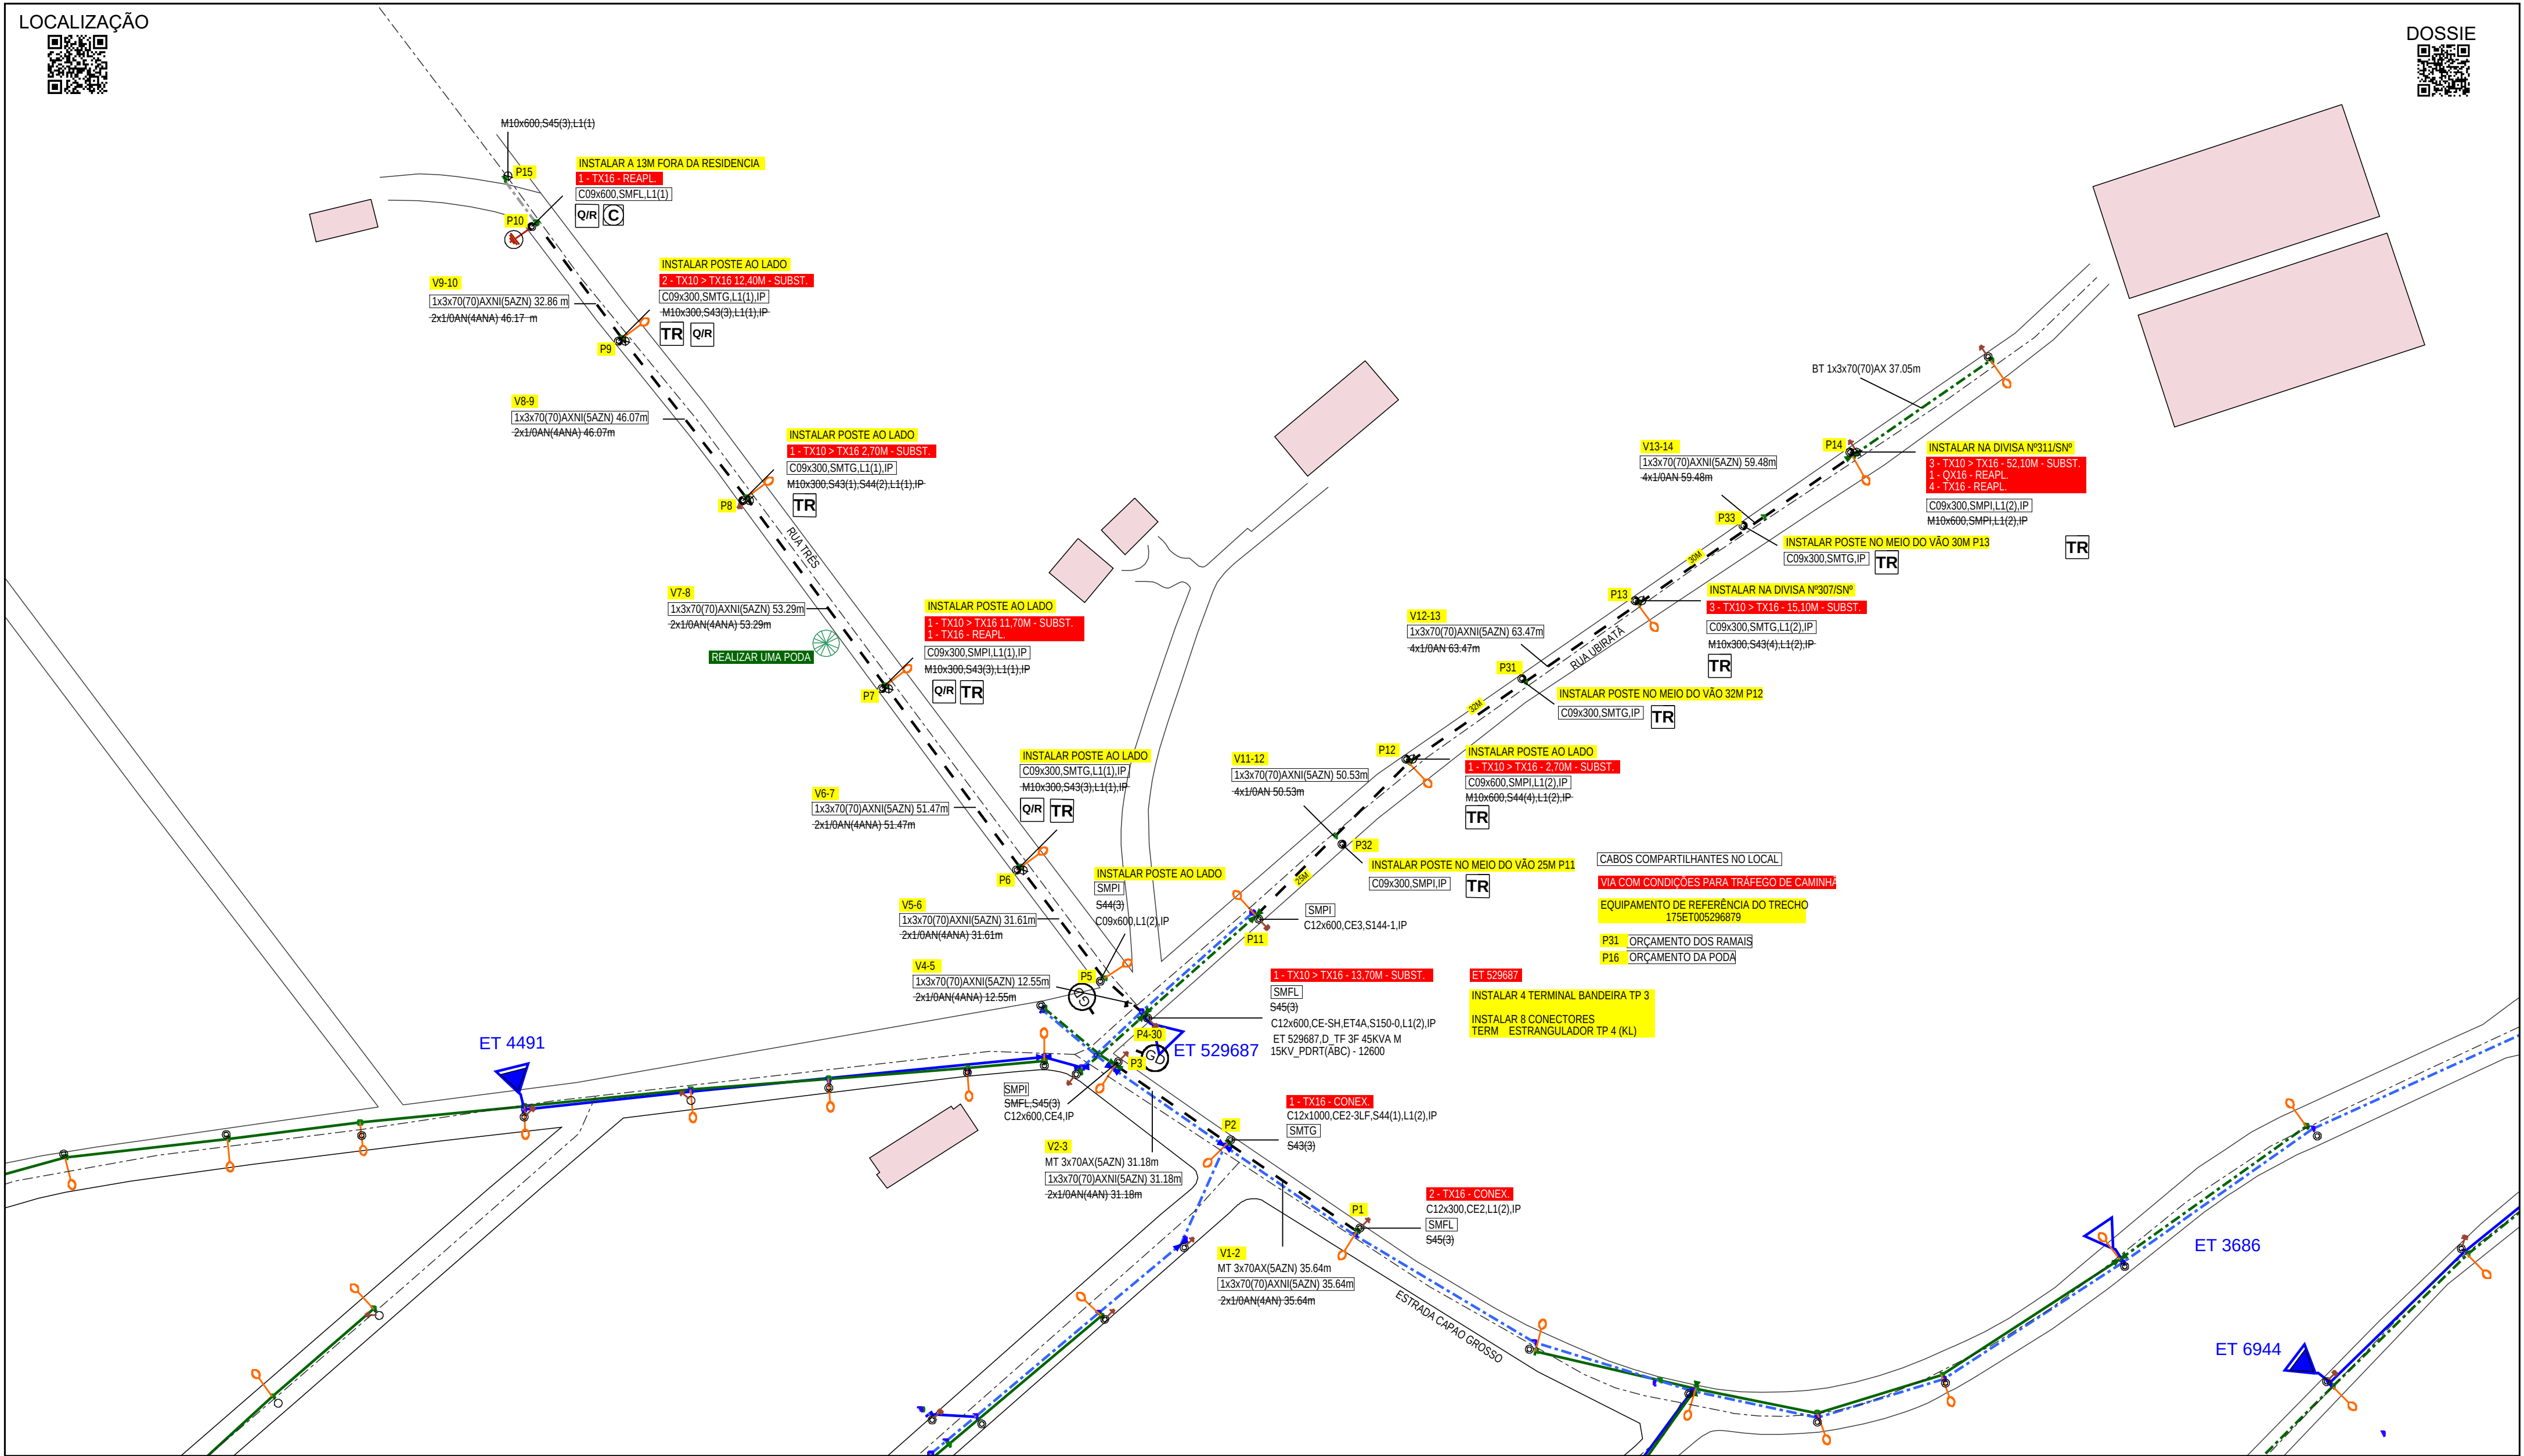

 REPARE E RECONSTRUA  RECONSTRUA E RECONSTRUA  USE CAPACETE  ANALISE ESCALA  USE LUVA  USE ATERAMENTO  SINALIZE VIA  TESTE A REDE  N											
CODIGO DO PROJETO				SOLICITANTE		EDP - SP					
16813660				ENDEREÇO		RUA UBIRATAN, 308					
				BAIRRO		CAPAO GROSSO					
						CIRCUITO		RPTE 1307			
						DISPOSITIVO		175ET005296879			
TITULO:		ELEMENTO PEP		DIAGRAMA		PROJETISTA		GUILHERME / ELI LUIZ			
CRUZETA REDE DE DISTRIBUIÇÃO - OPEX		16813660				DESENHISTA		ex162622			
MUNICIPIO:						DATA		26/03/2026			
SÃO JOSE CAMPOS				OBSERVAÇÕES		DESENHO 1 DE 1		OFICIO REF		A2	
CAMINHO DO PDF		\\vedpbr141\EORepository\ProjectPDF\16813660_Desenho_1_6.pdf				ESCALA		1:1000			