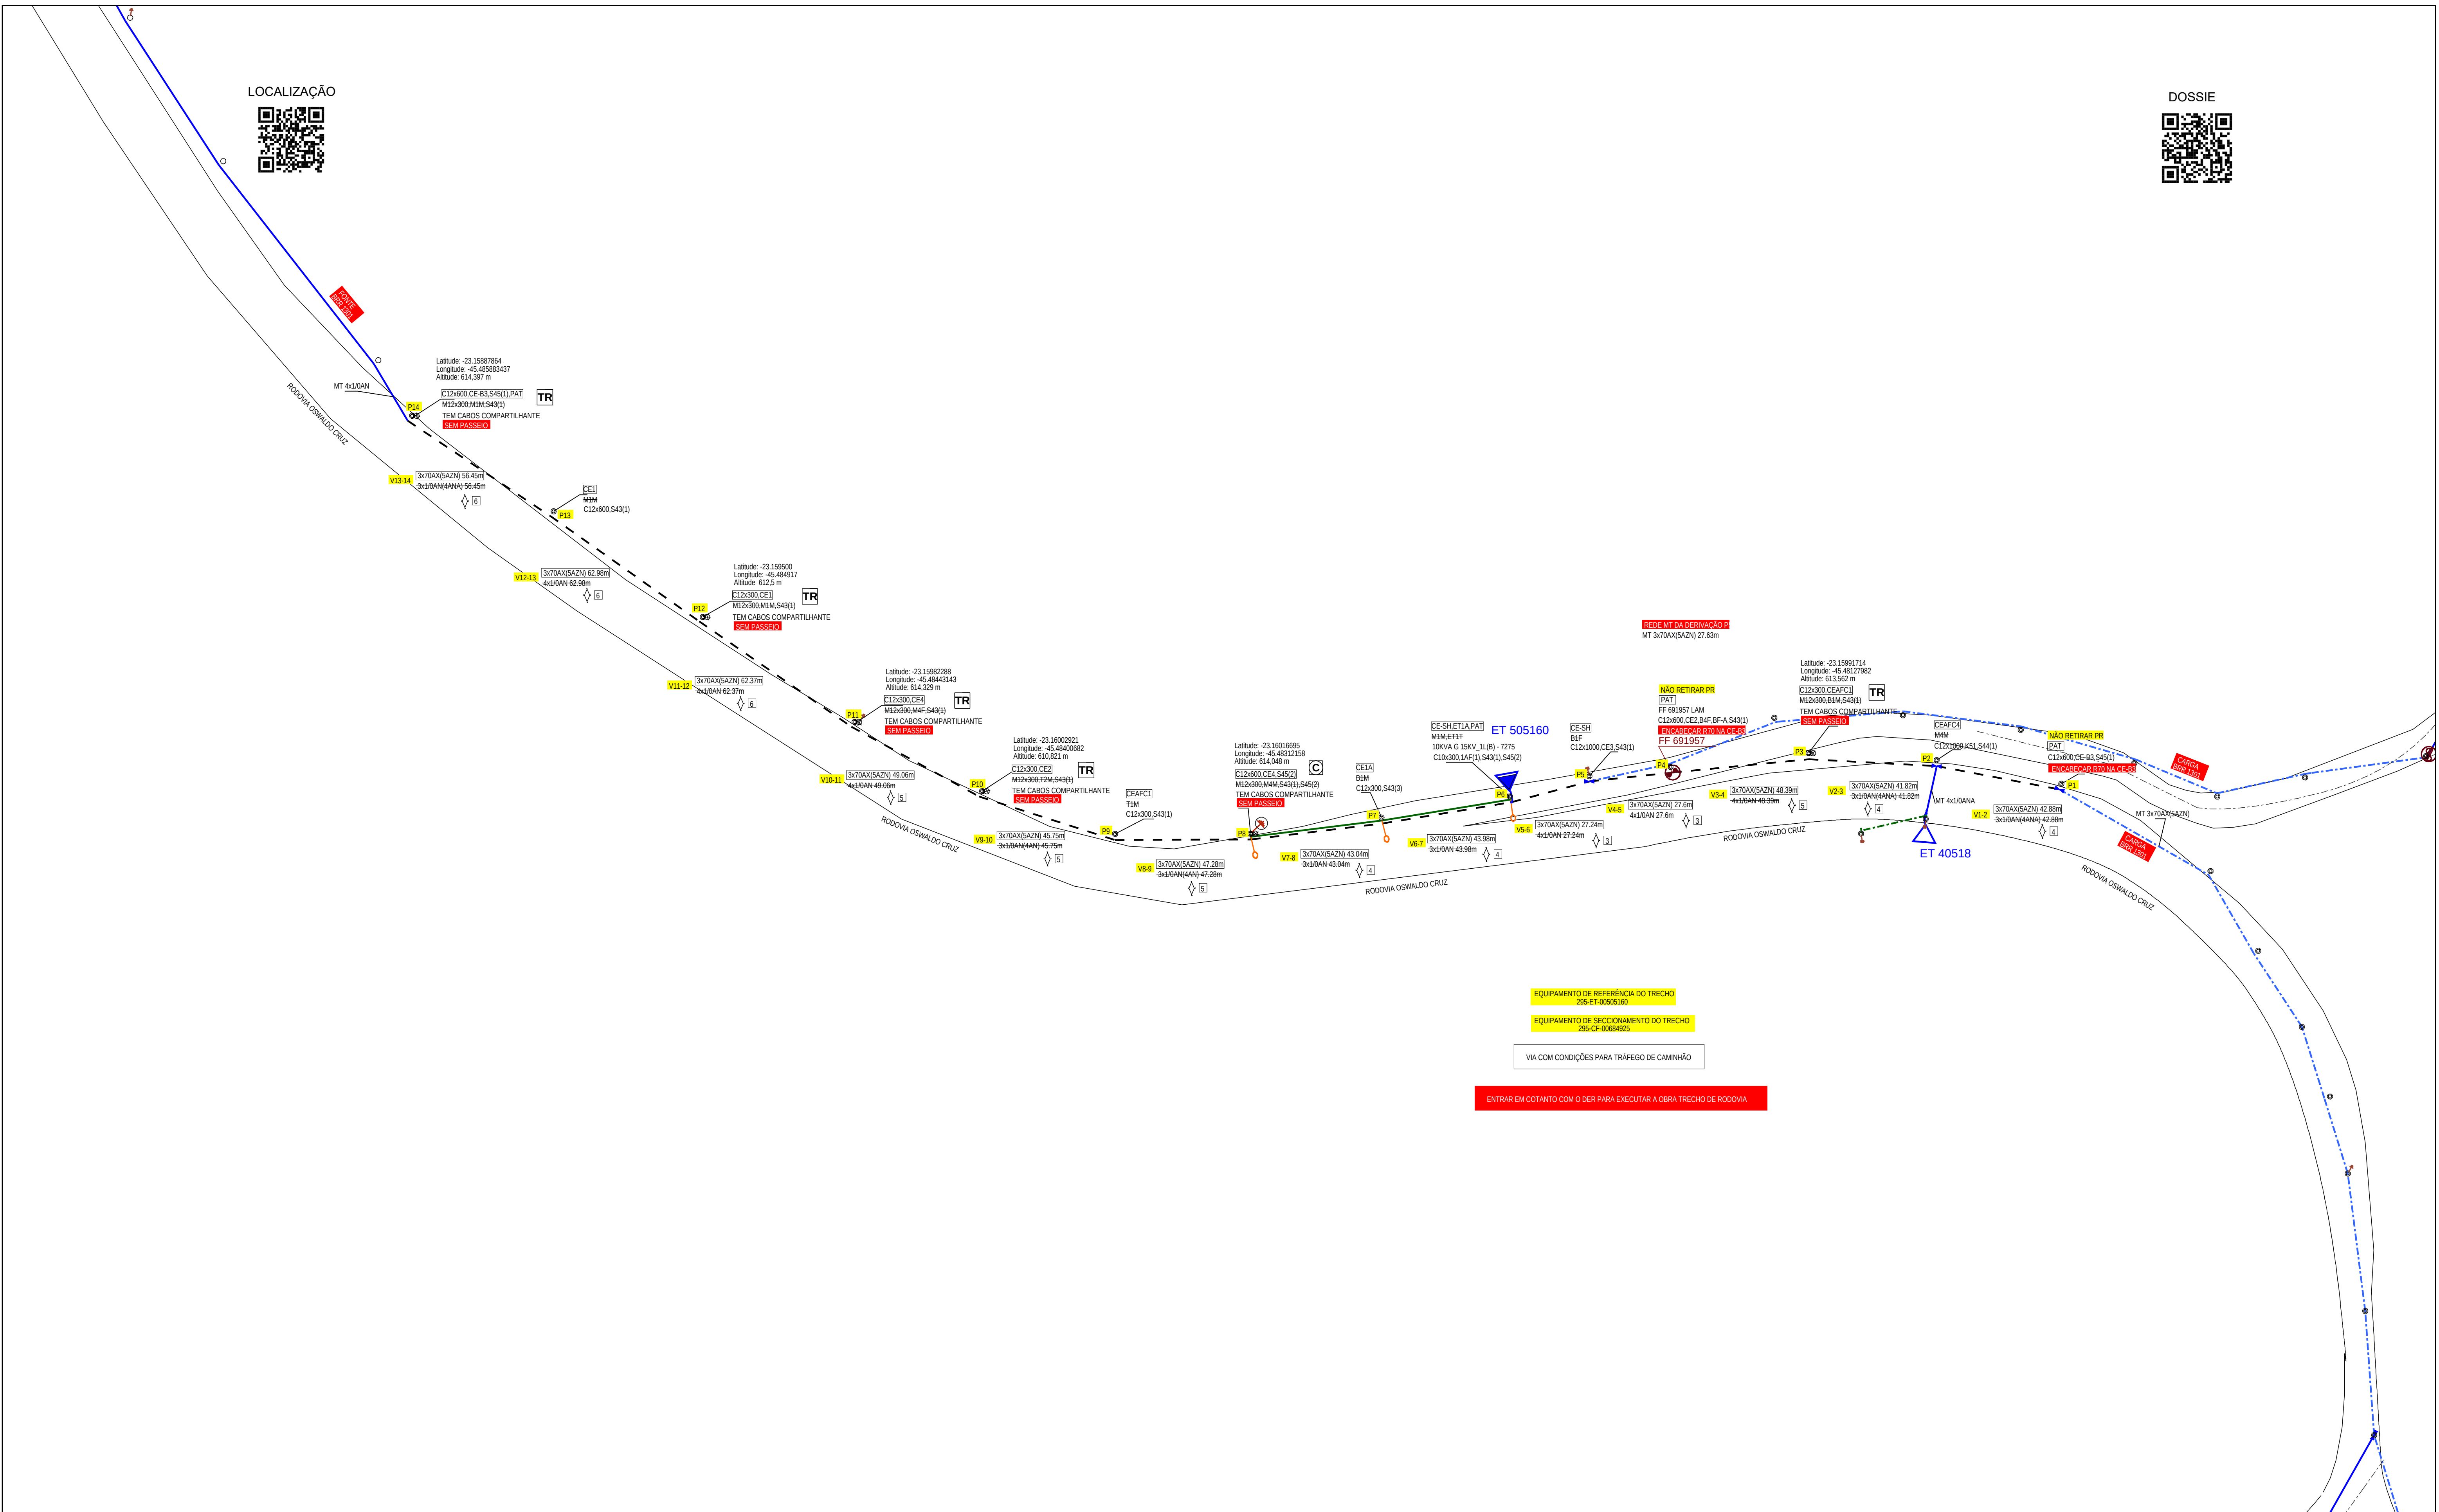


CÓDIGO DO PROJETO		SOLICITANTE		EDP-SP	
14858611		ENDEREÇO		RODOVIA OSWALDO CRUZ, S/N	
		BARRIO		REGISTRO	
		CIRCUITO		BRR 1301	
		DISPOSITIVO		295-ET-00505180	
REDE		ELEMENTO PEP		DIAGRAMA	
REDE COMPACTA PROTEGIDA - CAPEX		14858611		PROJETISTA	
MUNICÍPIO				DESENHISTA	
TALUOTE				DATA	
CAMINHO DO PDF		OBSERVAÇÕES		ORÇAO REF	
\\edp141\4\CRRepository\Project\PDF\14858611_Desenho_2_1.pdf				ESCALA	
				A1	
				1:1000	