


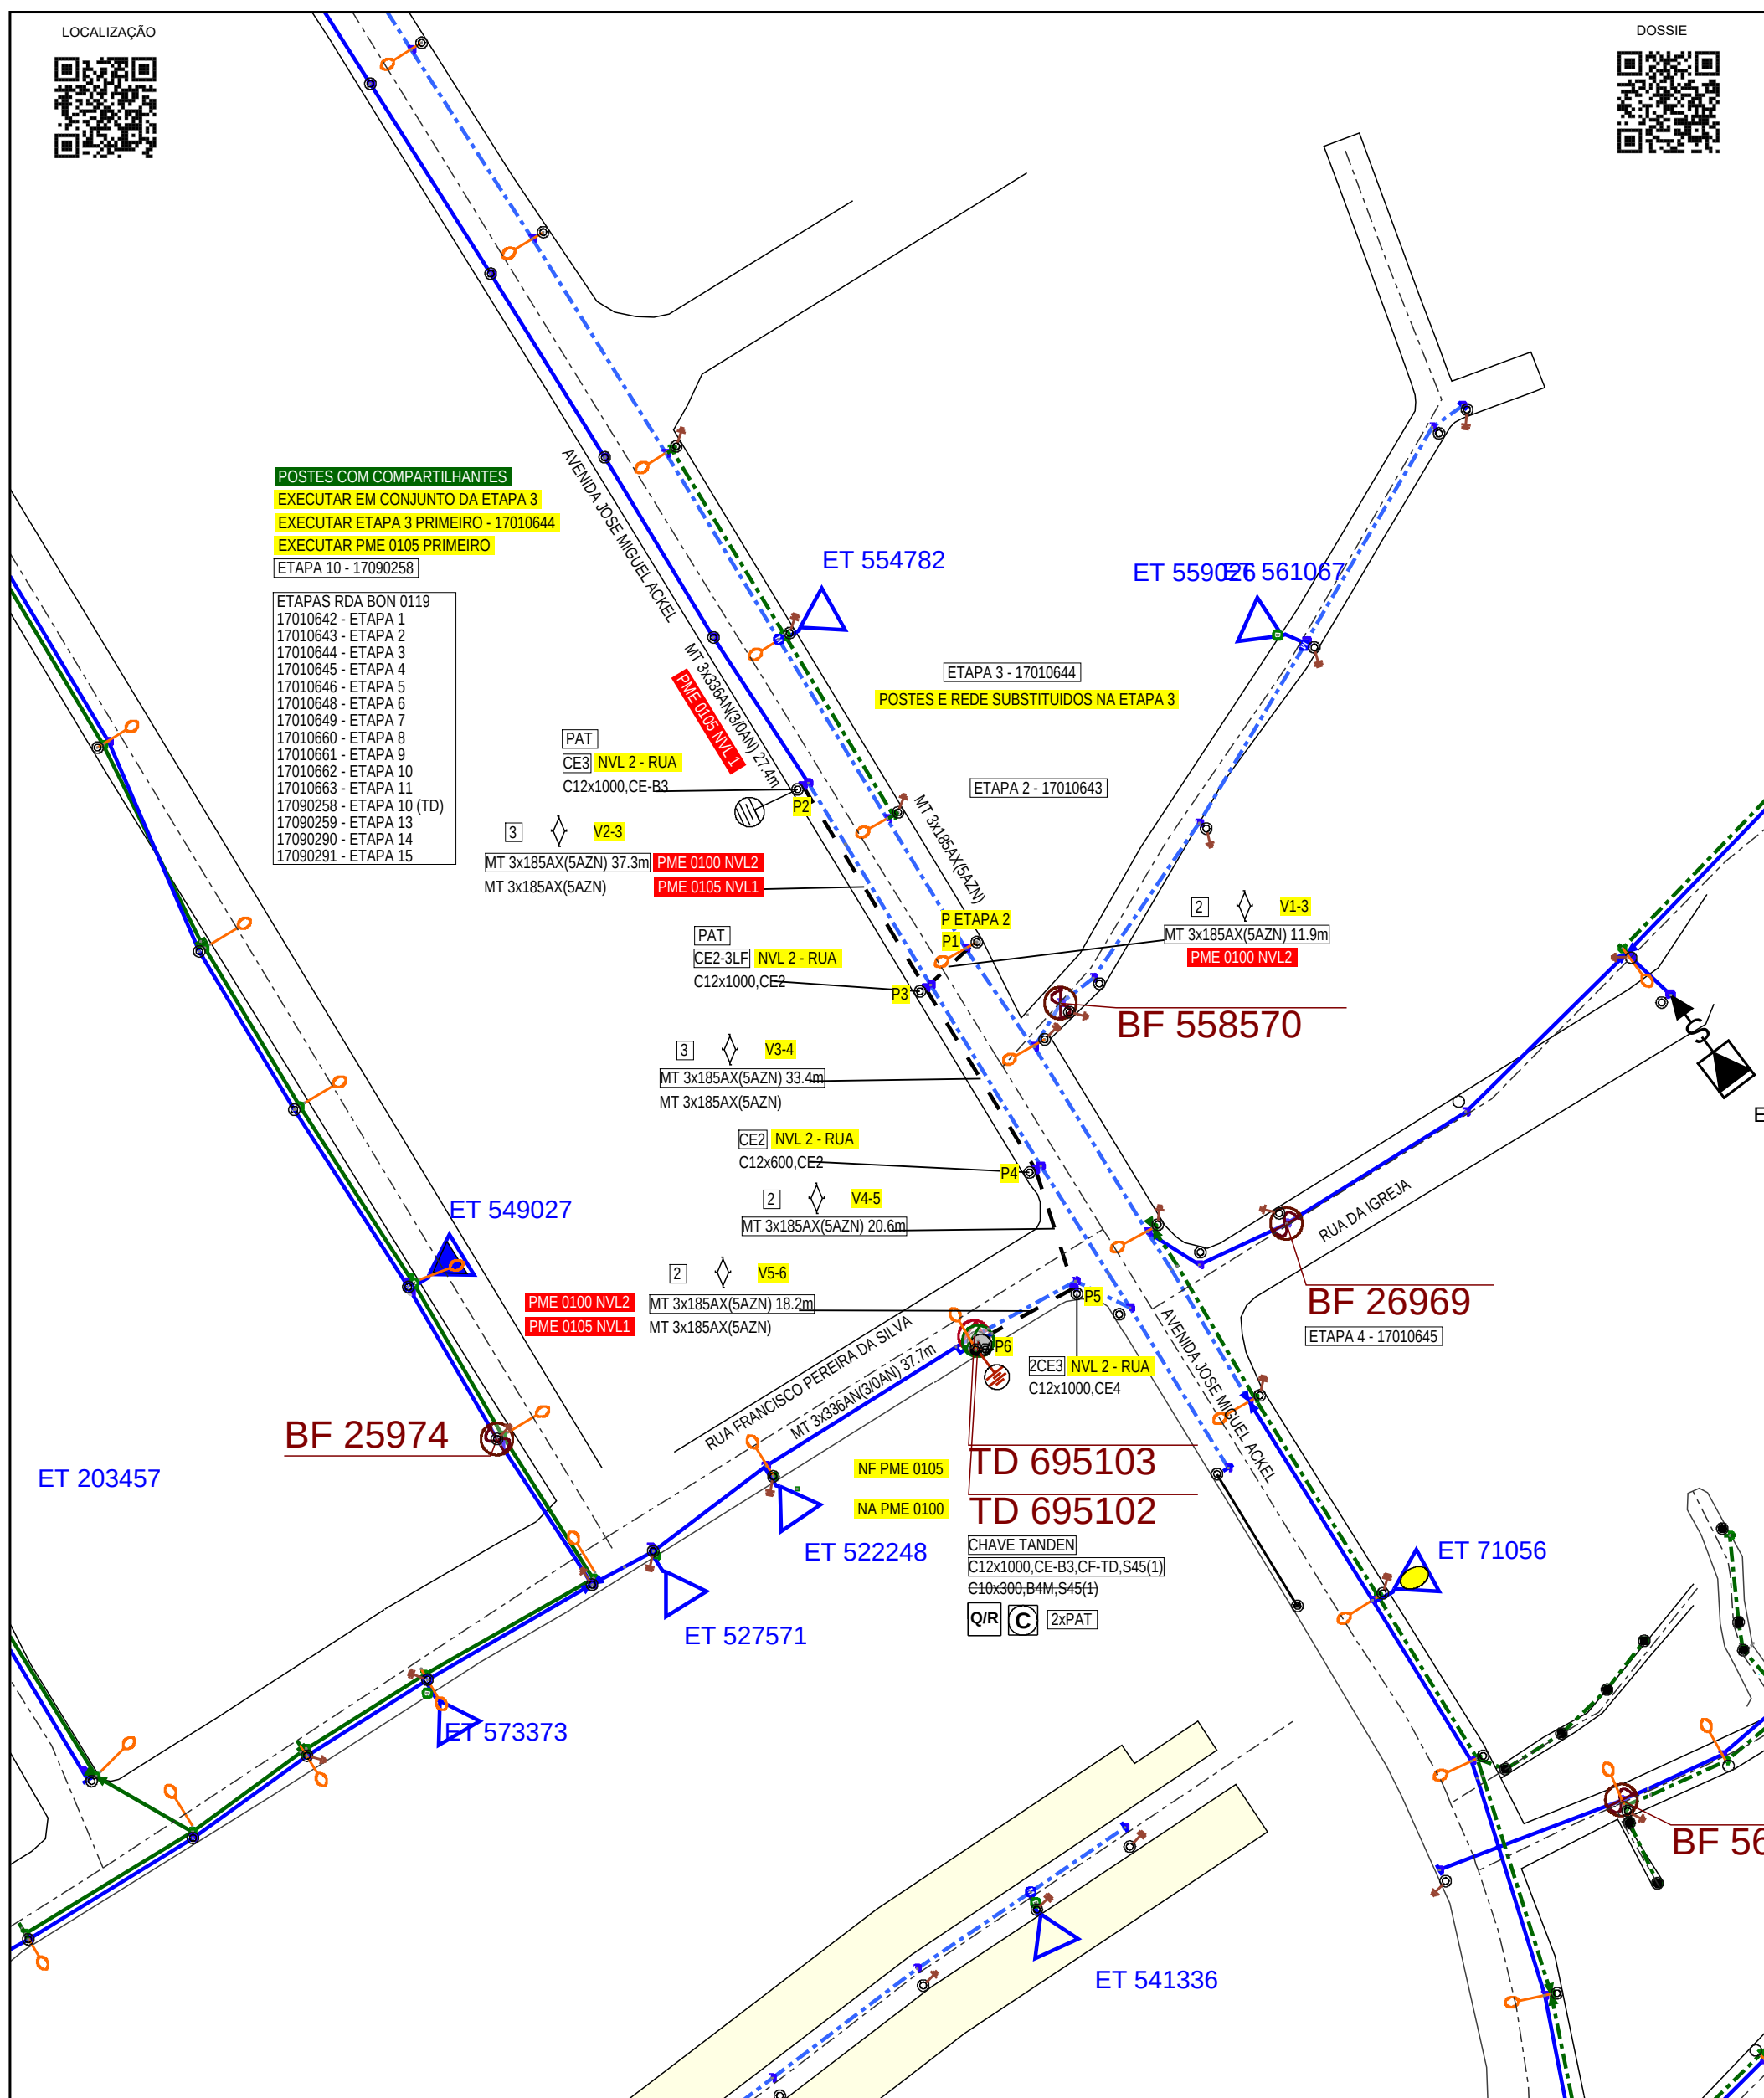

CODIGO DO PROJETO				SOLICITANTE		EDP SP					
17090258				ENDereco		AVENIDA JOSE MIGUEL ACKEL, 2637					
				BAIRRO		JARDIM MONTE ALEGRE					
						CIRCUITO		PME 0105			
						DISPOSITIVO		ET 522248			
TITULO:			ELEMENTO PEP		DIAGRAMA		PROJETISTA		GUILHERME / TIAGO		
POA - LDA - EXTENSÃO REDE DISTR. AÉREA			17090258				DESENHISTA		10006154		
MUNICIPIO:							DATA		29/05/2026		
GUARULHOS			OBSERVAÇÕES		ETAPA 10 - BON 0119			OFICIO REF		A3	
CAMINHO DO PDF		\\edpbr141\EORepository\ProjectPDF\17090258_Desenho 1_1.pdf					ESCALA		1:1000		